ВЕРТИКАЛЬ

СРО-П-179-12122012

625002 Россия г. Тюмень, ул. Свердлова д. 5 корп. 2, офис 207;
Тел. +7-9044-76-66-36; www.vertikal72.com; mail@vertikal72.com

Объект: Комплекс многоэтажных жилых домов с нежилыми помещениями, Тюменский район, объездная дорога ул. Мельникайте - ул. Широтная. Жилой дом ГП-18

Раздел: Паспорт фасада


Директор: А. С. Аксенов

ГИП: А. С. Аксенов

Тюмень 2020

Ведомость рабочих чертежей основного комплекта

Лист	Наименование	Примечание
1	Ситуационный план	
2	План благоустройства	
3	Фасад 1-11. Фасад 11-1	
4	Фасад И-А. Фасад А-И	
5	План 1-го этажа. Вход в нежилое помещение. Вход в жилую часть здания	
6	План типового этажа. Устройство парапета	
7	Перспективный вид	

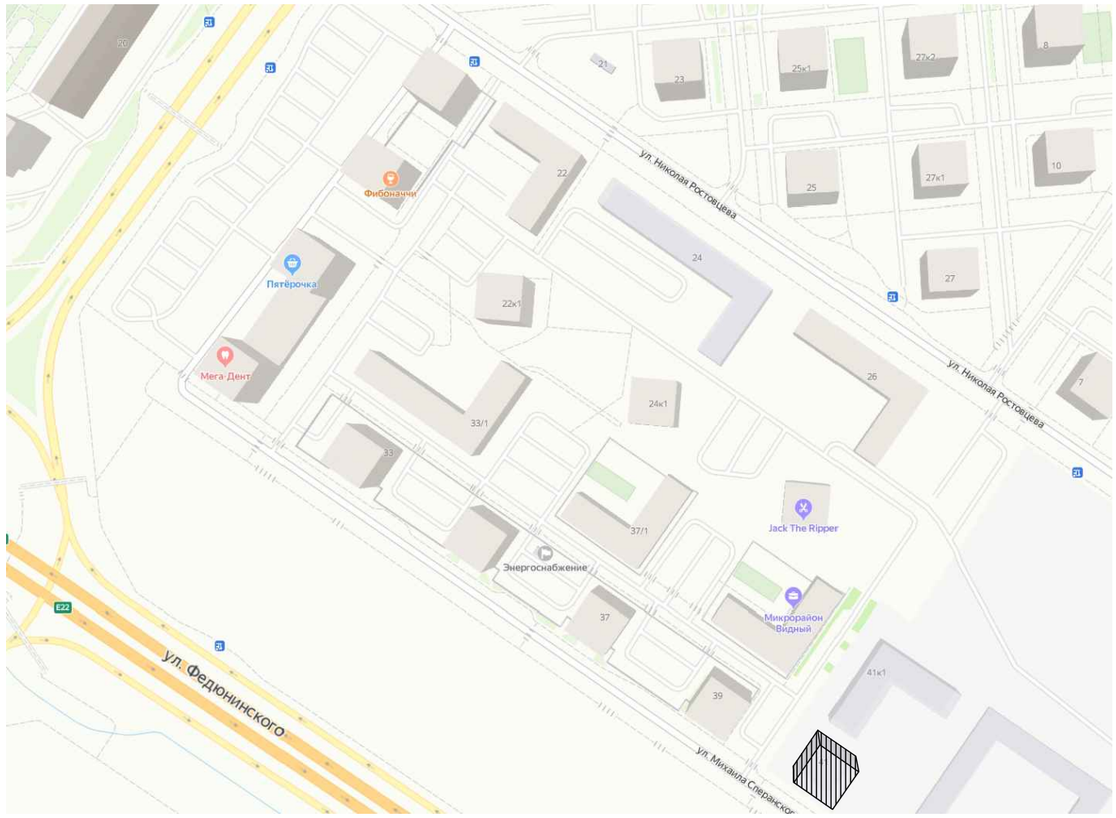

Описание и обоснование использованных композиционных приемов при оформлении фасадов объекта капитального строительства.

Архитектурно-художественный образ здания решен в современном европейском стиле, созвучным со стилевыми решением существующей застройки. Архитектурная выразительность достигается благодаря сочетанию горизонтальных и вертикальных членений, подчеркивающих тектонику здания, сочетанием глухих и остекленных плоскостей, цветовых решений фасадов.

Наружной отделкой здания предусмотрено:

- В качестве отделочного материала жилого дома предусмотрено применение штукатурки.
- Окна в нежилых помещениях алюминиевые стоечно-ригельные.
- Окна в жилых помещениях по ГОСТ 30674-99, из поливинилхлоридного профиля с заполнением двухкамерным стеклопакетом.
- Наружные двери входных групп в здание, алюминиевые, остекленные.


Примечание:
Разработка паспорта фасадов здания, в том числе его цветовое решение осуществляется в соответствии с требованиями постановления Администрации города Тюмень от 14 мая 2012 г. N 51-пк "Об утверждении порядка и условий составления изменения и согласования паспорта фасадов зданий, строений и сооружений на территории города Тюмени".

Изм.	Кол.уч.	Лист	N док.	Подп.	Дата	Паспорт фасада			
						Комплекс многоэтажных жилых домов с нежилыми помещениями, Тюменский район, объездная дорога ул. Мельникайте – ул. Широтная. Жилой дом ГП-18			
Разраб.		Денисова			11.20		Стадия	Лист	Листов
Проверил		Стрепетилов			11.20			1	7
Общие данные							ВЕРТИКАЛЬ		

Взам. инв. N°
Подпись и дата
Инв. N° подл.

Формат А3

ПЛАН БЛАГОУСТРОЙСТВА. М 1:500

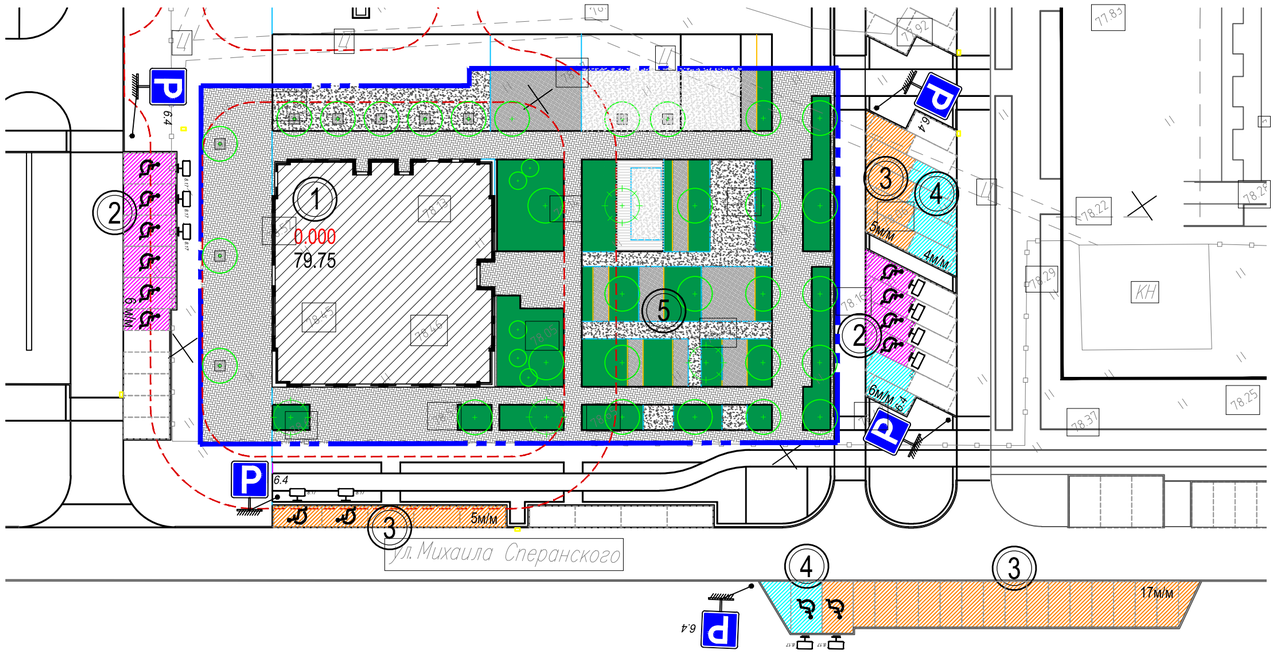

Экспликация зданий и сооружений

Номер по плану	Наименование	Примечание
1	Многоквартирный 18-ти этажный жилой дом	V очередь
2	Автостоянки	
3	Гостевые автостоянки	
4	Временные автостоянки	
5	Площадка для отдыха	

Ведомость элементов озеленения

Поз	Наименование породы или вида насаждения	воз-раст, лет.	Кол-во, шт. ГП 18	Примечание
1	Лиственное дерево		30	
2	Хвойное дерево		4	
3	Кустарники солитеры		5	
4	Газон обыкновенный, цветники из однолетних цветов(м) ^{2}		774,32	

Ведомость нормируемых элементов территории

Номер на плане	Нормируемые элементы территории	Площадь, м ^{2} по проекту ГП- 18	нормативный показатель: показатель на одного человека, м2тер.чел	нормативный показатель: всего ГП- 18
2	Автостояки	3 (101 м/м паркинг)	По расчету. См. Лист- 2, 3	(116х 0.9) 104
3	Гостевые автостоянки	26	По расчету. См. Лист- 2, 3	(104х0.25) 26
4	Временные автостоянки	7	По расчету. См. Лист- 2, 3	(331.25/100) * 4/2 5
	Спортивные площадки	-	2 (1- прим.1,таблицы А1, Региональных нормативов)	217.00
	Площадки для игр детей дошкольного и младшего школьного возраста	-	0.7	151.90
	Площадки для отдыха взрослого населения	-	0,1	21.70
5	Хозяйственные площадки	135.20	0.3	65.10
	Площадка для размещения мусорных контейнеров	-	По расчету. См. Лист- 2	-
	Площадка для выгула собак	См. прим.2	0,3 кв.м/чел СЗЗ 40м	65.10
	Участки зелёных насаждений	774.32	4.5	922.5

Условные обозначения

- Граница участка
- Проектируемые здания сооружения
- Проезды
- Тротуар
- Автостоянки постоянного хранения
- Временные автостоянки
- Гостевые автостоянки
- М/м для хранения автомобилей МГН
- Площадки для отдыха
- Озеленение

Ведомость дорожных знаков

Условное изображение	№ ГОСТ	Количество, шт.	Наименование
ГОСТ Р 52 290- 2004. Знаки дорожные			
	6.4	4	Место стоянки (II категория) d700
	8.17	7	Инвалиды (II категория) 350*700
ГОСТ Р 51 256- 2011. Разметка дорожная			
	1.24.3	7	Дублирование знака дополнительной информации 8.17 "Инвалиды"

1. При комплексном освоении территории микрорайона расчет потребности в нормируемых площадях выполнен в границах территории. Лист смотреть совместно с листами ПЗУ-2 и ПЗУ-6.
Проектом предусмотрено размещение недостающего количества площадок на смежных земельных участках, т.к. территория запроектирована комплексно в границах проектируемого микрорайона.

2. Согласно табл. А1, часть 3, прим.3 допускается организация общей для одного или нескольких микрорайонов оборудованной площадки для выгула собак на территории вне жилой застройки в радиусе до 500 м.

Изм.	Кол.уч.	Лист	Nдок.	Подп.	Дата	Паспорт фасада
						Комплекс многоэтажных жилых домов с нежилыми помещениями, Тюменский район, объездная дорога ул. Мельникайте-ул. Широтная Жилой дом ГП-18
Выполнил		Лебенштейн			11.20	Стадия: — Лист: 2 Листов: —
Проверил		Кирьянов			11.20	План благоустройства М1:500
Н.контроль		Баранов			11.20	ООО "АКБ "Куб-А"

Согласовано

Взам. инв. N


Подп. и дата

Инв. N подл.


Копировал

Формат А2

Фасад 1-11

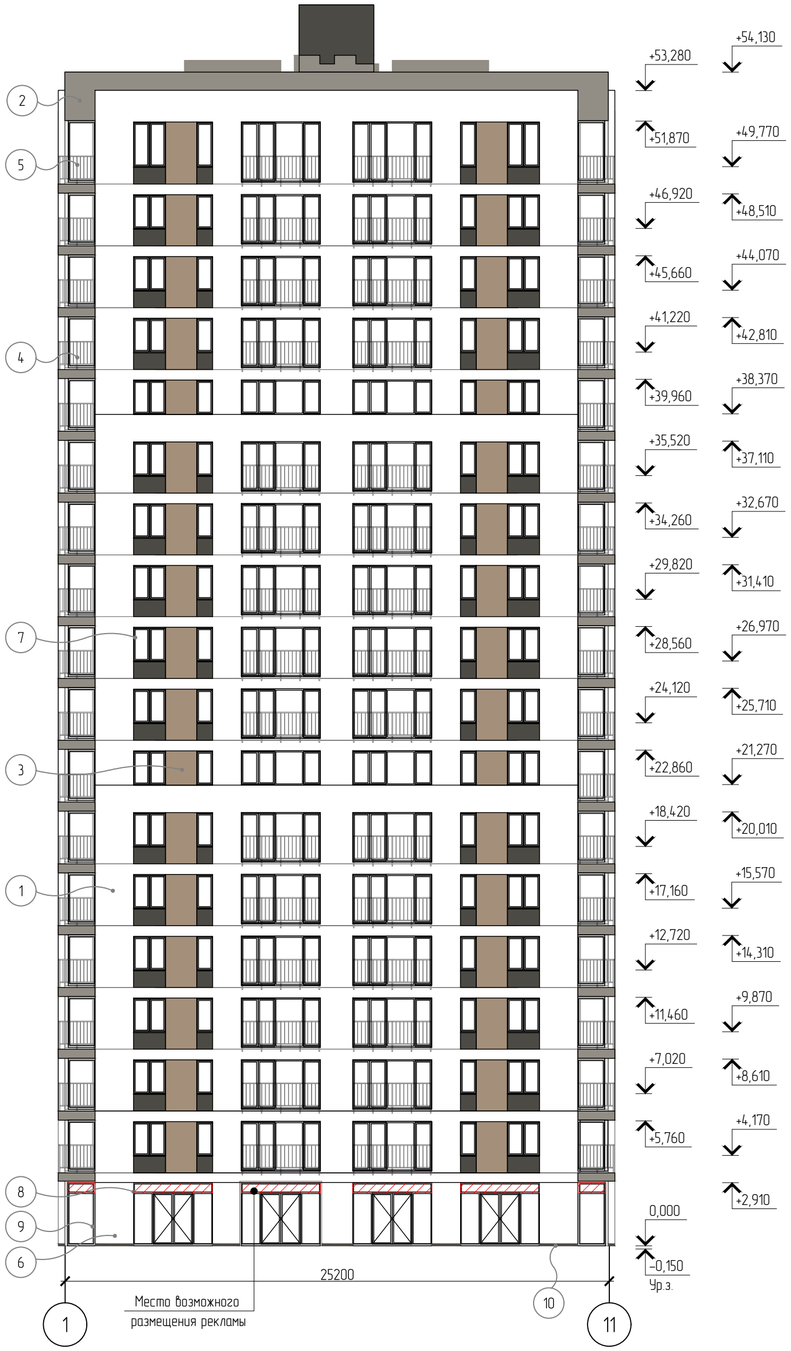

Фасад 11-1

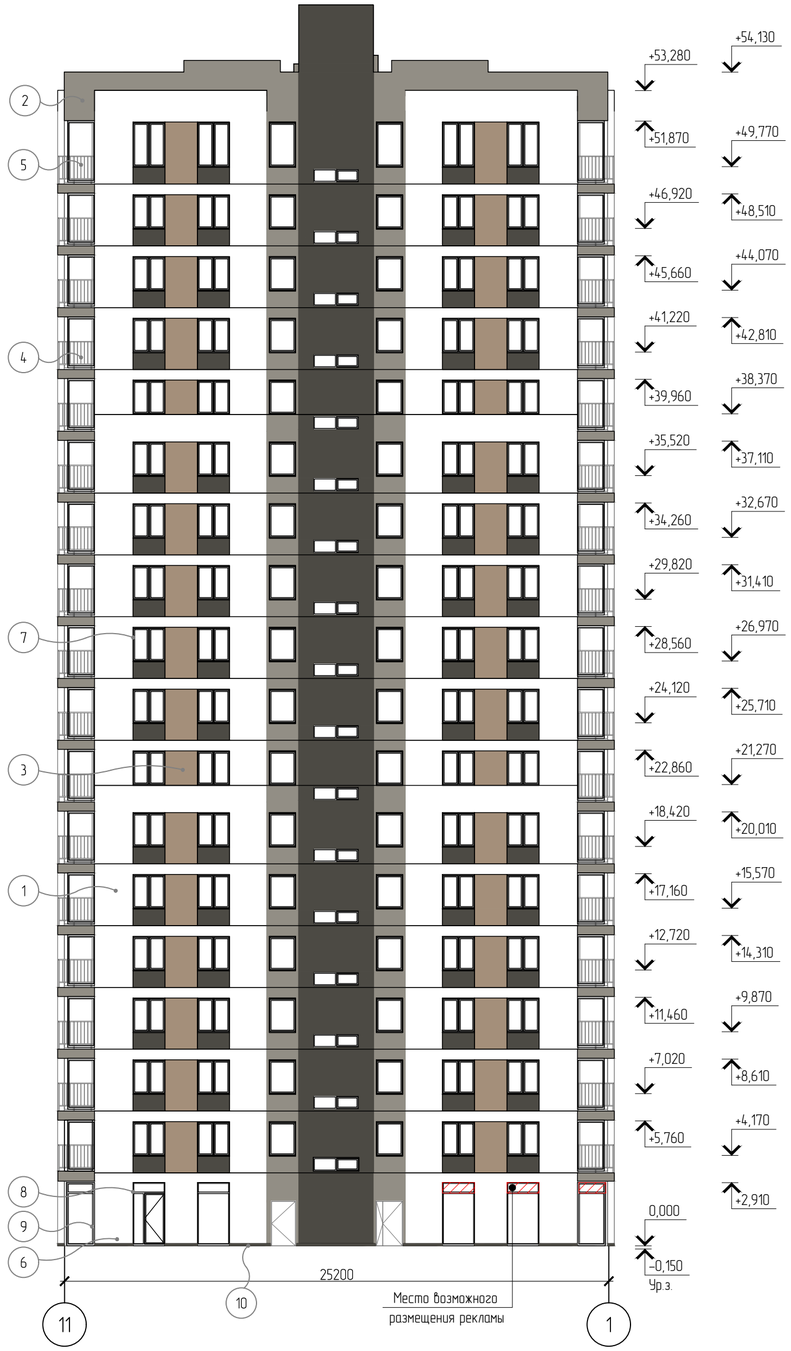

Ведомость отделки фасадов

N п.п	Отделываемая поверхность	Вид отделки	N колера	Эталон колера
1	Поверхность фасада	Тонкослойная фасадная штукатурка	RAL 9001	
2	Поверхность фасада	Тонкослойная фасадная штукатурка	RAL 7030	
3	Поверхность фасада	Тонкослойная фасадная штукатурка (или фасадная панель)	RAL 1019	
4	Поверхность фасада	Тонкослойная фасадная штукатурка (или фасадная панель)	RAL 7022	
5	Ограждение лоджий	Металлическое окрашенное	RAL 7022	
6	Поверхность фасада	Тонкослойная фасадная штукатурка (или фасадная панель)	RAL 9001	
7	Окна	ПВХ-профиль	RAL 7022	
8	Двери	Алюминиевый профиль	RAL 7022	
9	Окна	Алюминиевый профиль	RAL 7022	
10	Цоколь	Цокольная штукатурка	RAL 7022	

* Поверхность фасада под номером 4 - выполнить с толщиной утеплителя 120 мм.
* Поверхность фасада под номером 3 - выполнить с толщиной утеплителя 180 мм.

Взам. инв. №

Подпись и дата

Инв. № подл.

Изм.	Кол.уч.	Лист	N док.	Подп.	Дата
Разраб.		Денисова			11.20
Проверил		Стрепетилов			11.20

Паспорт фасада

Комплекс многоэтажных жилых домов с нежилыми помещениями, Тюменский район, объездная дорога ул. Мельникайте - ул. Широтная. Жилой дом ГП-18


Стадия	Лист	Листов
	2	

Фасад 1-11. Фасад 11-1


ВЕРТИКАЛЬ

Формат А2

Фасад 1-11

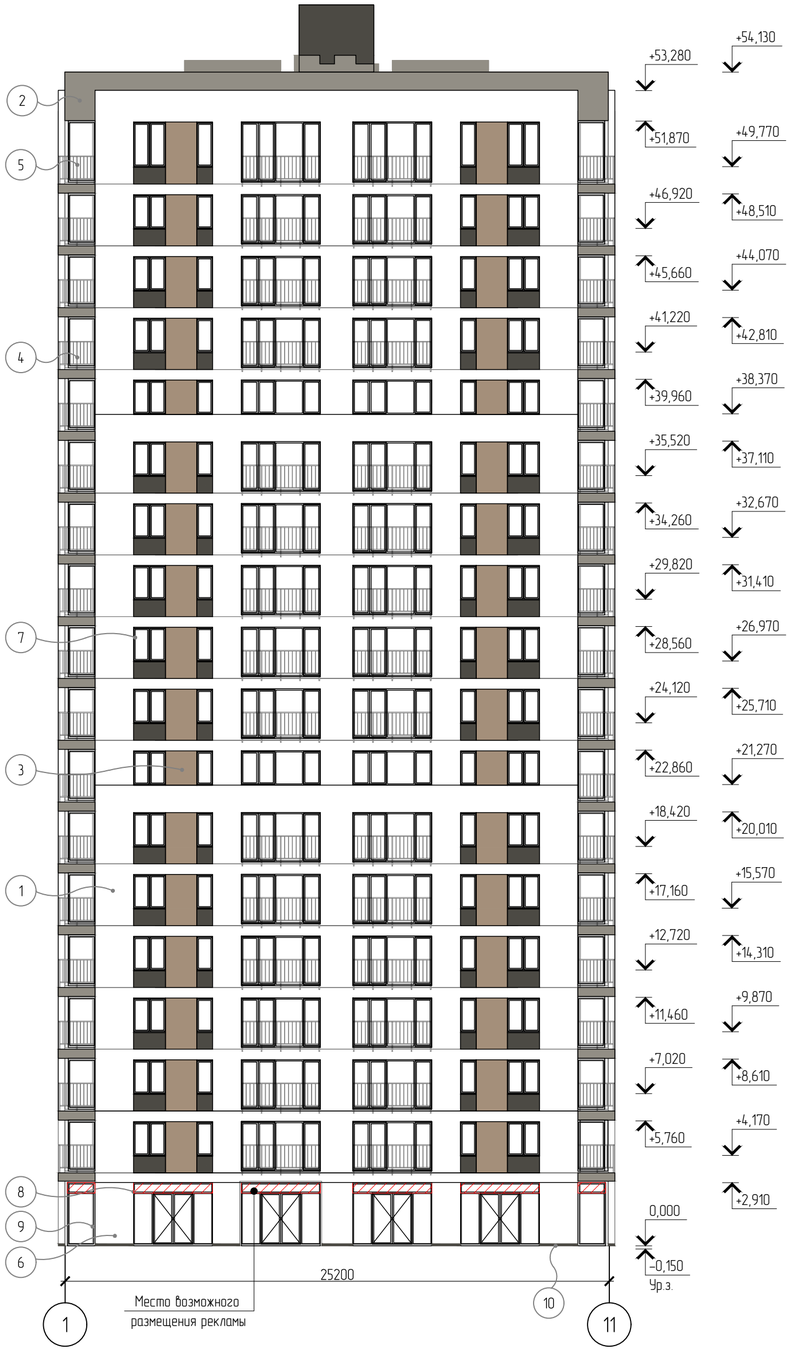

Фасад 11-1

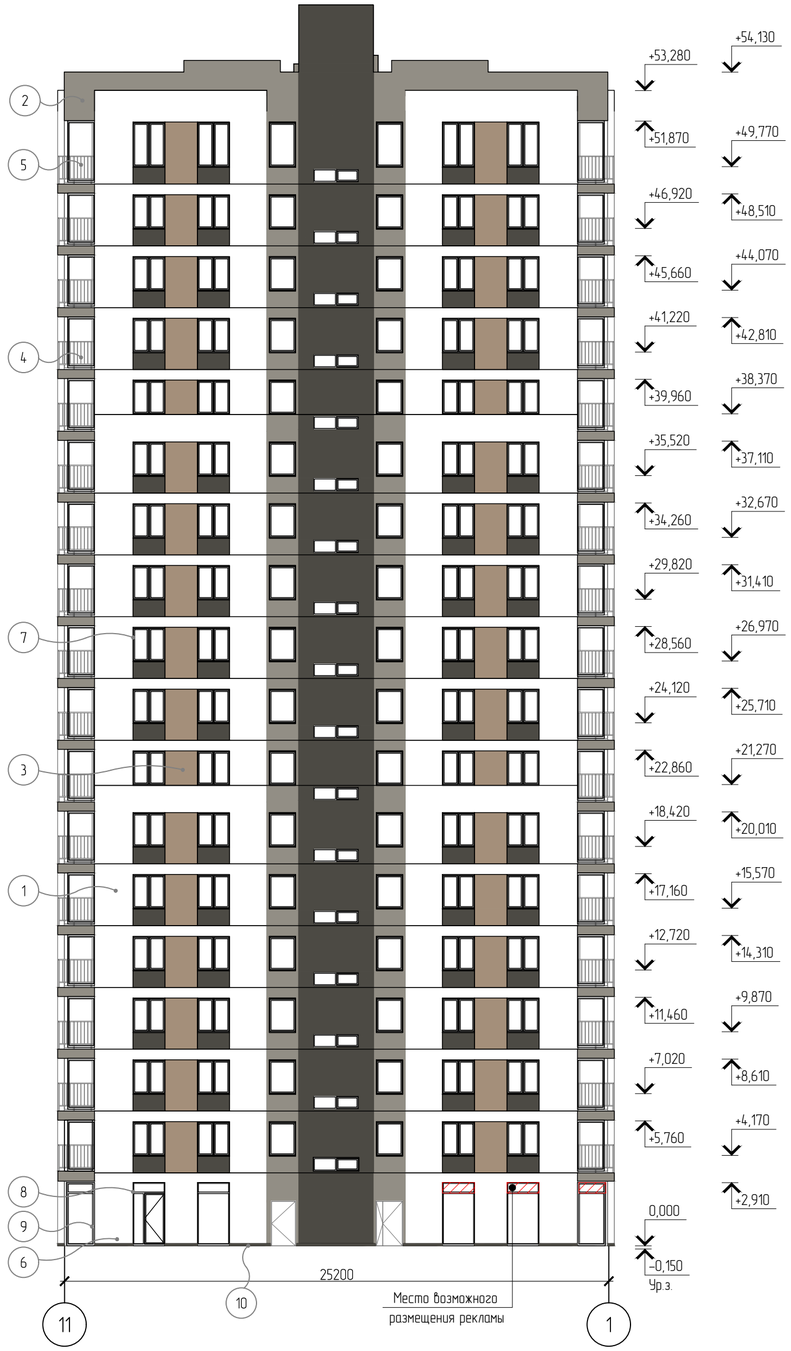

Ведомость отделки фасадов

N п.п	Отделываемая поверхность	Вид отделки	N колера	Эталон колера
1	Поверхность фасада	Тонкослойная фасадная штукатурка	RAL 9001	
2	Поверхность фасада	Тонкослойная фасадная штукатурка	RAL 7030	
3	Поверхность фасада	Тонкослойная фасадная штукатурка (или фасадная панель)	RAL 1019	
4	Поверхность фасада	Тонкослойная фасадная штукатурка (или фасадная панель)	RAL 7022	
5	Ограждение лоджий	Металлическое окрашенное	RAL 7022	
6	Поверхность фасада	Тонкослойная фасадная штукатурка (или фасадная панель)	RAL 9001	
7	Окна	ПВХ-профиль	RAL 7022	
8	Двери	Алюминиевый профиль	RAL 7022	
9	Окна	Алюминиевый профиль	RAL 7022	
10	Цоколь	Цокольная штукатурка	RAL 7022	

* Поверхность фасада под номером 4 - выполнить с толщиной утеплителя 120 мм.
* Поверхность фасада под номером 3 - выполнить с толщиной утеплителя 180 мм.

Взам. инв. №

Подпись и дата

Инв. № подл.

Изм.	Кол.уч.	Лист	N док.	Подп.	Дата
Разраб.		Денисова			11.20
Проверил		Стрепетилов			11.20

Паспорт фасада

Комплекс многоэтажных жилых домов с нежилыми помещениями, Тюменский район, объездная дорога ул. Мельникайте - ул. Широтная. Жилой дом ГП-18


Стадия	Лист	Листов
	4	

Фасад И-А. Фасад А-И

ВЕРТИКАЛЬ

Формат А2

План 1-го этажа

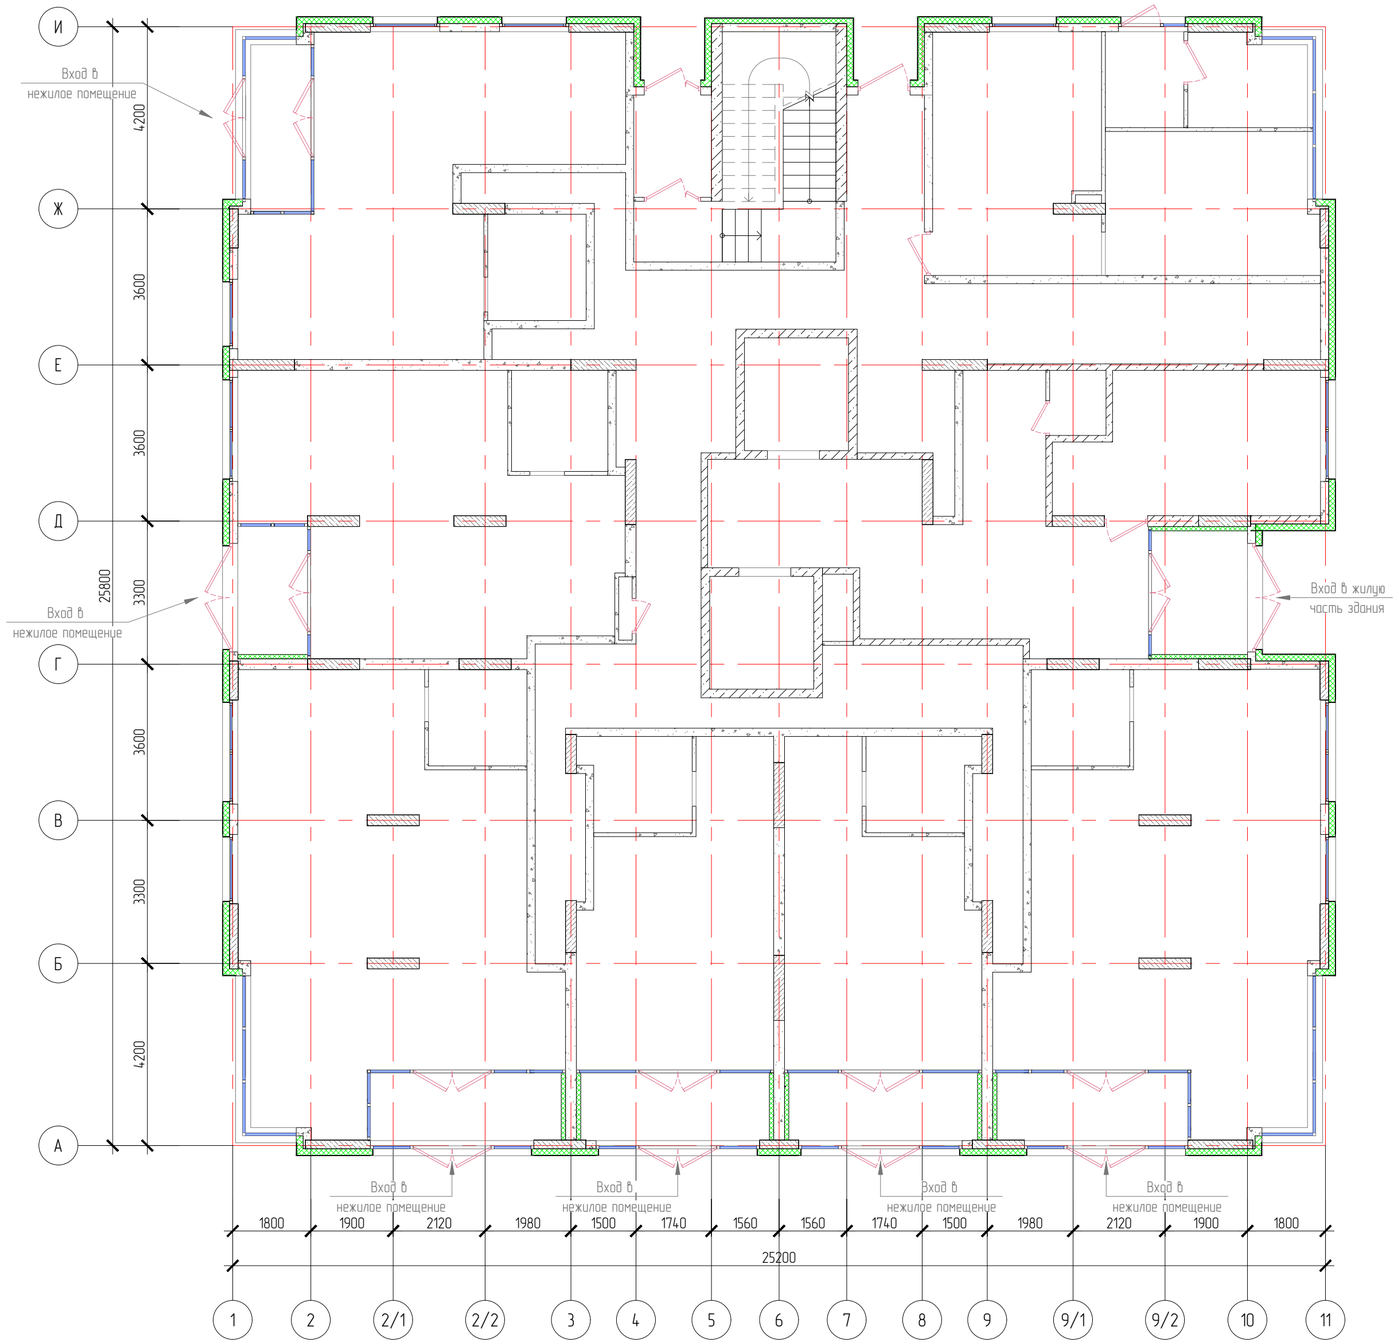

Вход в нежилое помещение



Вход в жилую часть здания



						Паспорт фасада
						Комплекс многоэтажных жилых домов с нежилыми помещениями, Тюменский район, объездная дорога ул. Мельникайте – ул. Широтная. Жилой дом ГП-18
Изм.	Кол.уч.	Лист	N док.	Подп.	Дата	
Разраб.		Денисова			11.20	Стадия: — / Лист: 5 / Листов: —
Проверил		Стрепетилов			11.20	
						План 1-го этажа. Вход в нежилое помещение. Вход в жилую часть здания
						ВЕРТИКАЛЬ


Взам. инв. №

Подпись и дата

Инв. № подл.

Формат А2

План типового этажа

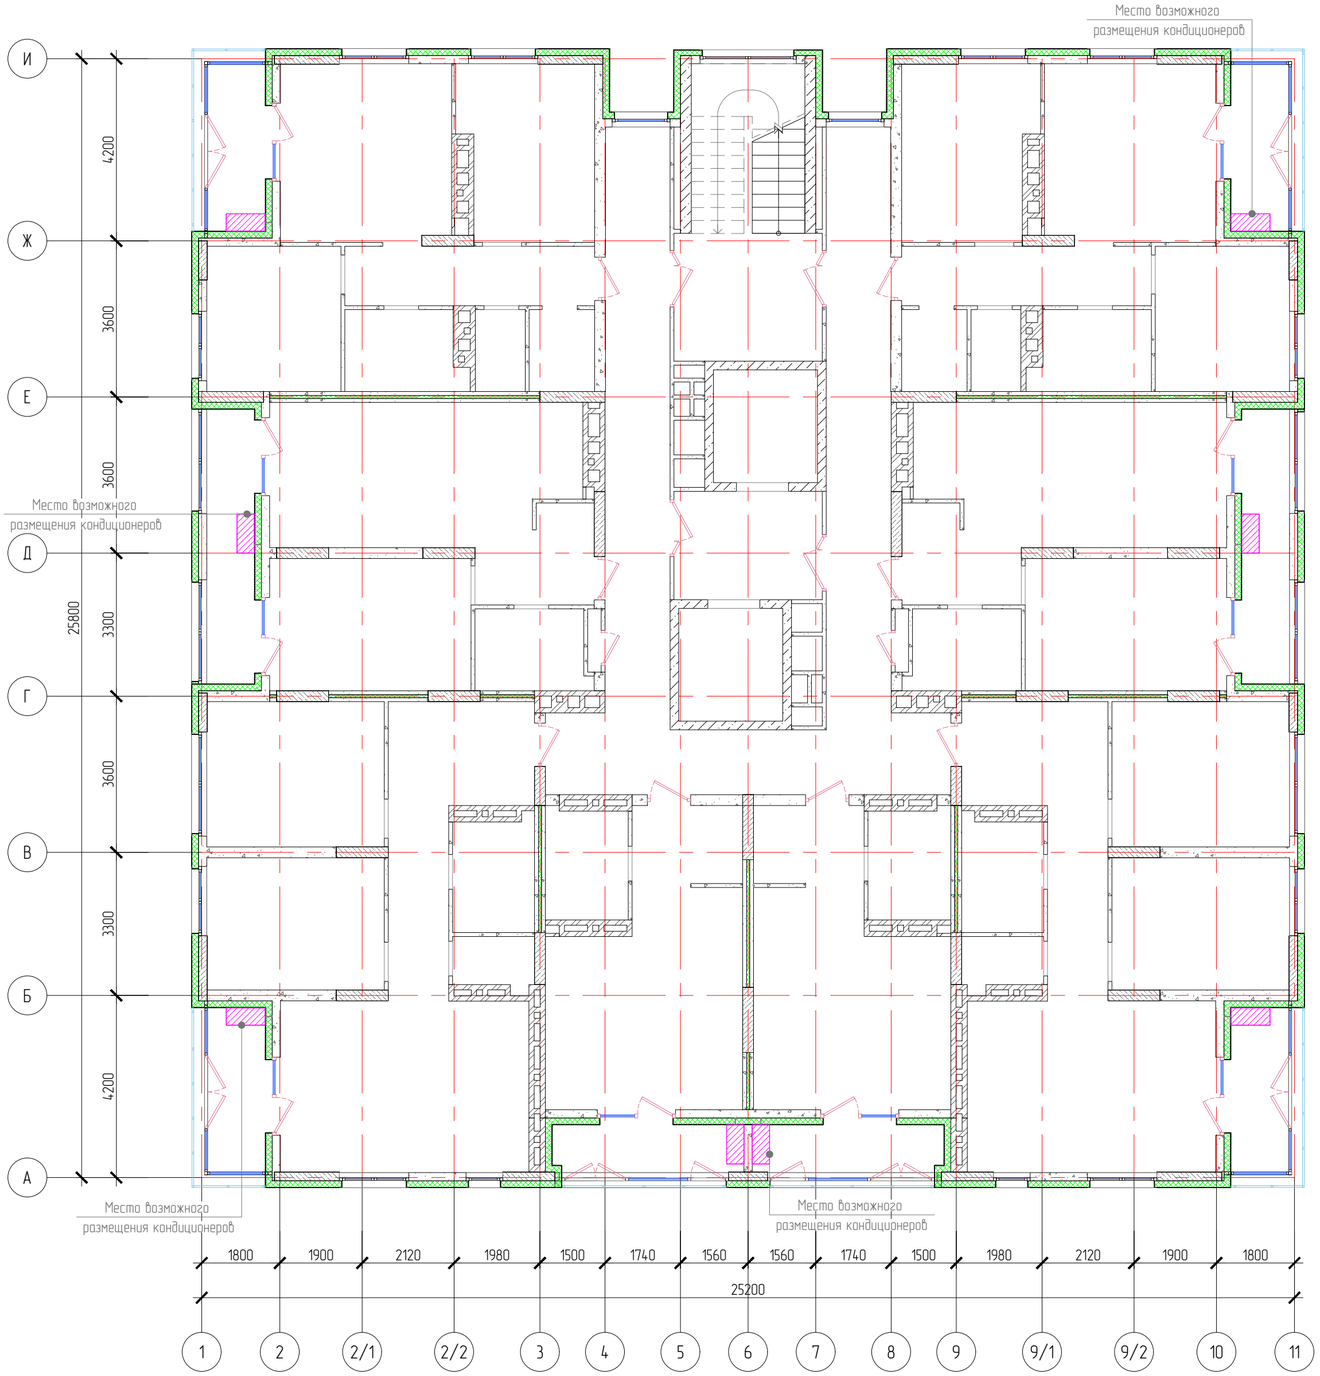

Устройство парапета



Изм.	Кол.уч.	Лист	N док.	Подп.	Дата
Разраб.		Денисова			11.20
Проверил		Стрепетилов			11.20

Паспорт фасада

Комплекс многоэтажных жилых домов с нежилыми помещениями, Тюменский район, объездная дорога ул. Мельникайте – ул. Широтная. Жилой дом ГП-18

Стадия	Лист	Листов
	6	

План типового этажа. Устройство парапета

ВЕРТИКАЛЬ


Формат А2

Взам. инв. №

Подпись и дата

Инв. № подл.

Перспективный вид

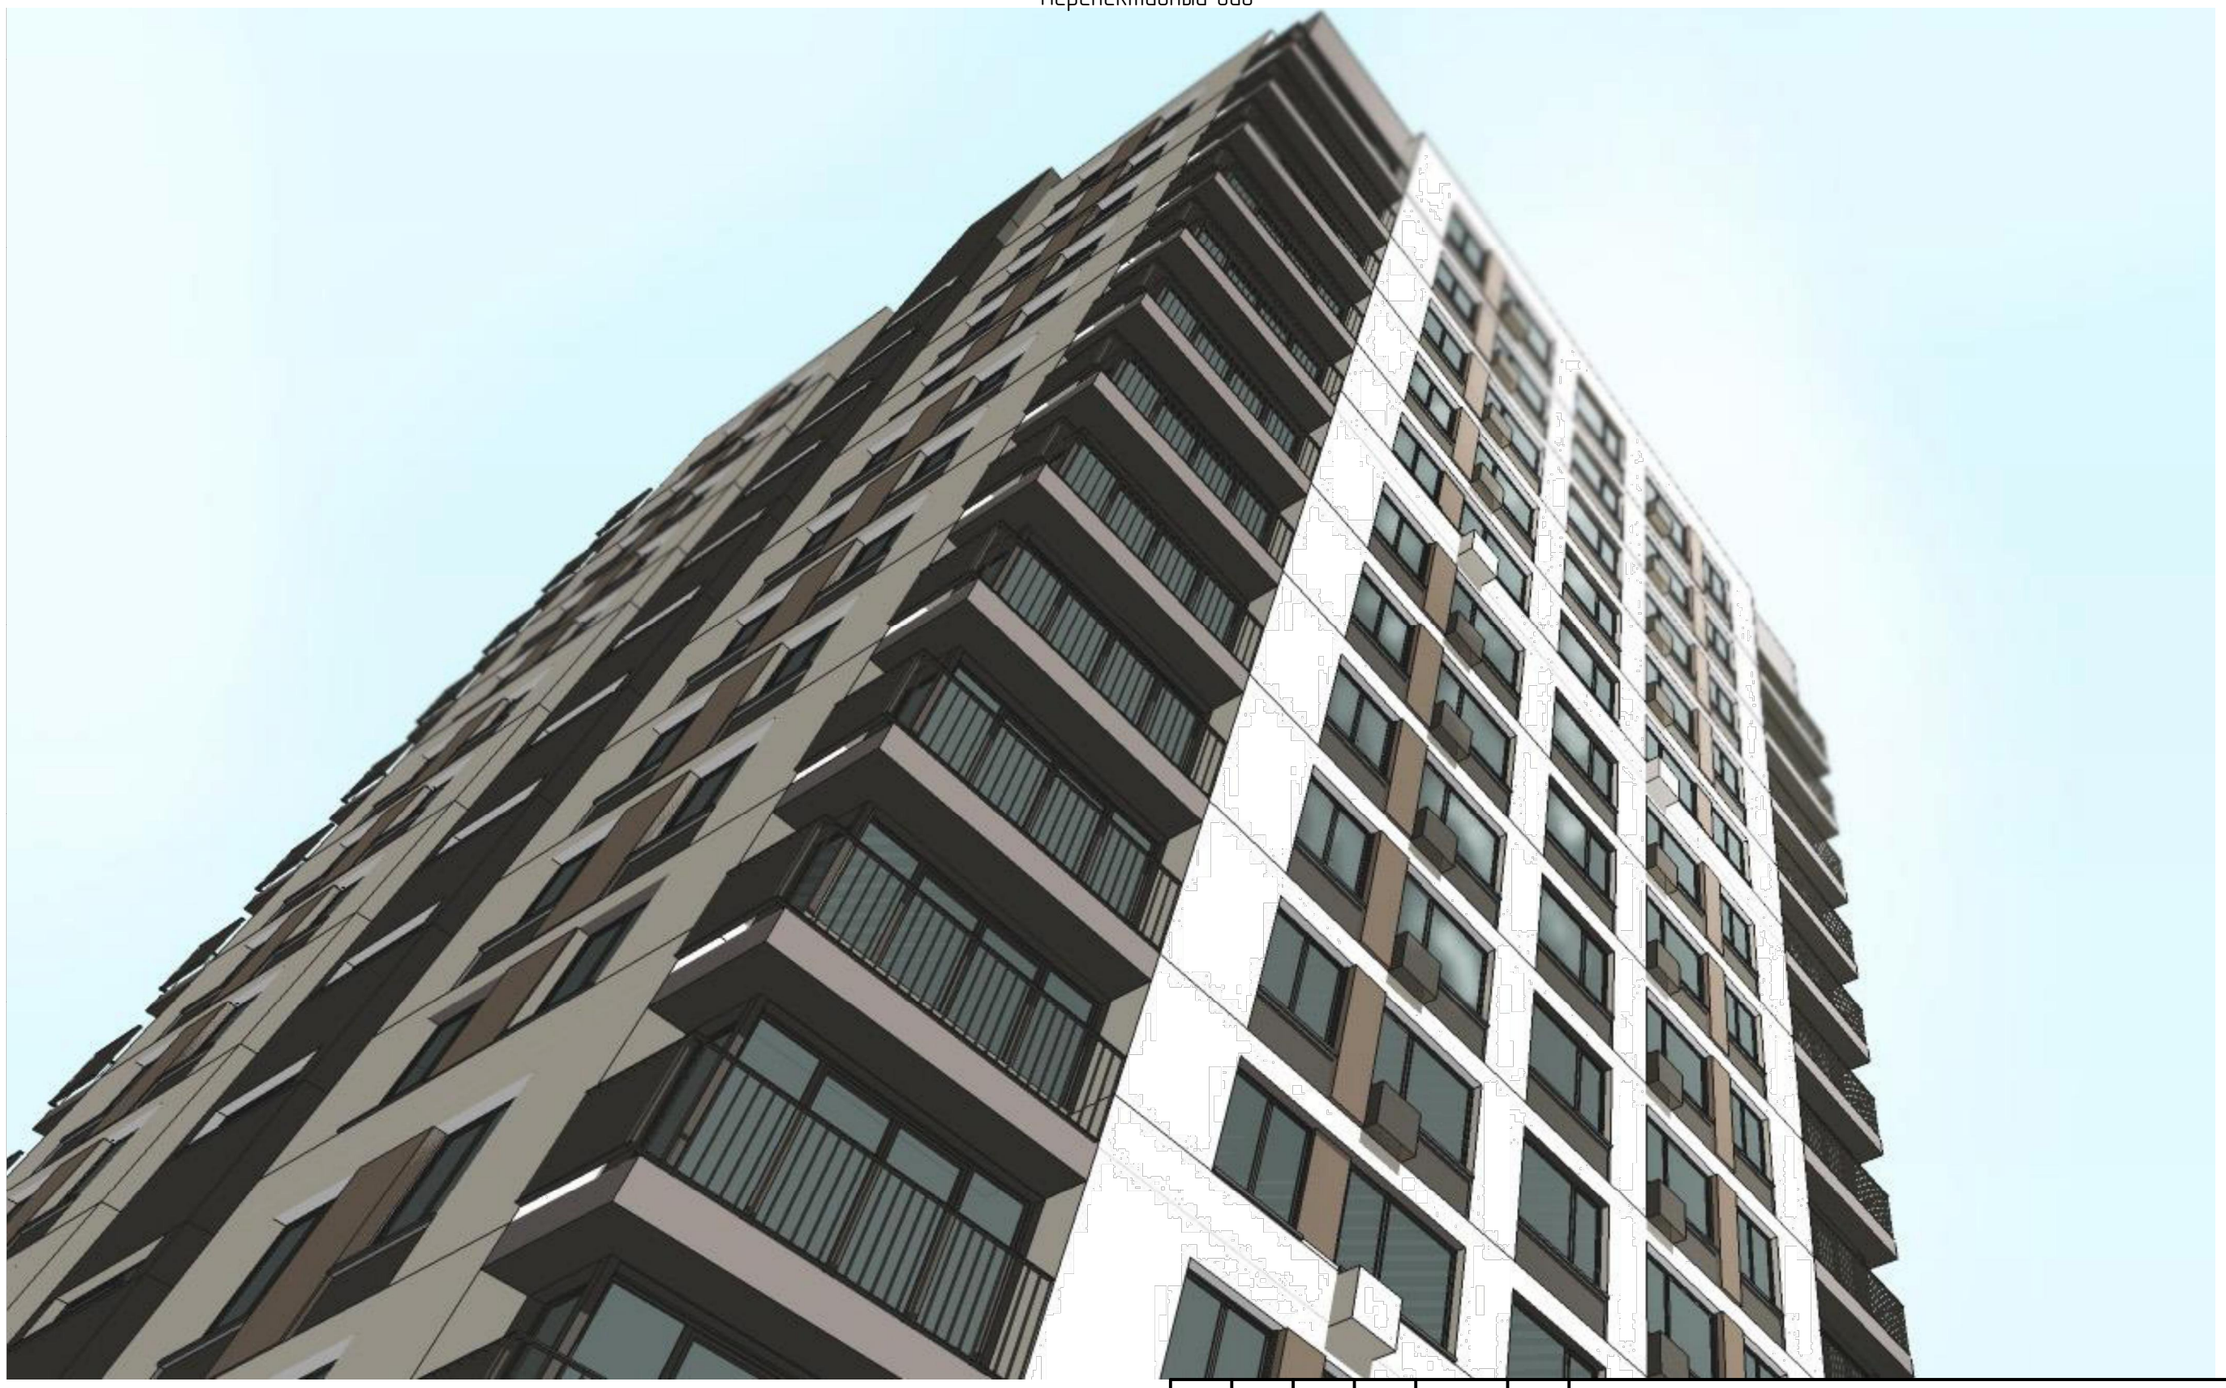

Взам. инв. №	
Подпись и дата	
Инв. № подл.	

Изм.	Кол.уч.	Лист	N док.	Подп.	Дата
Разраб.		Денисова			11.20
Проверил		Стрепетилов			11.20

Паспорт фасада

Комплекс многоэтажных жилых домов с нежилыми помещениями, Тюменский район, объездная дорога ул. Мельникайте – ул. Широтная. Жилой дом ГП-18

Стадия	Лист	Листов
	7	

Перспективный вид

ВЕРТИКАЛЬ

Формат А3